

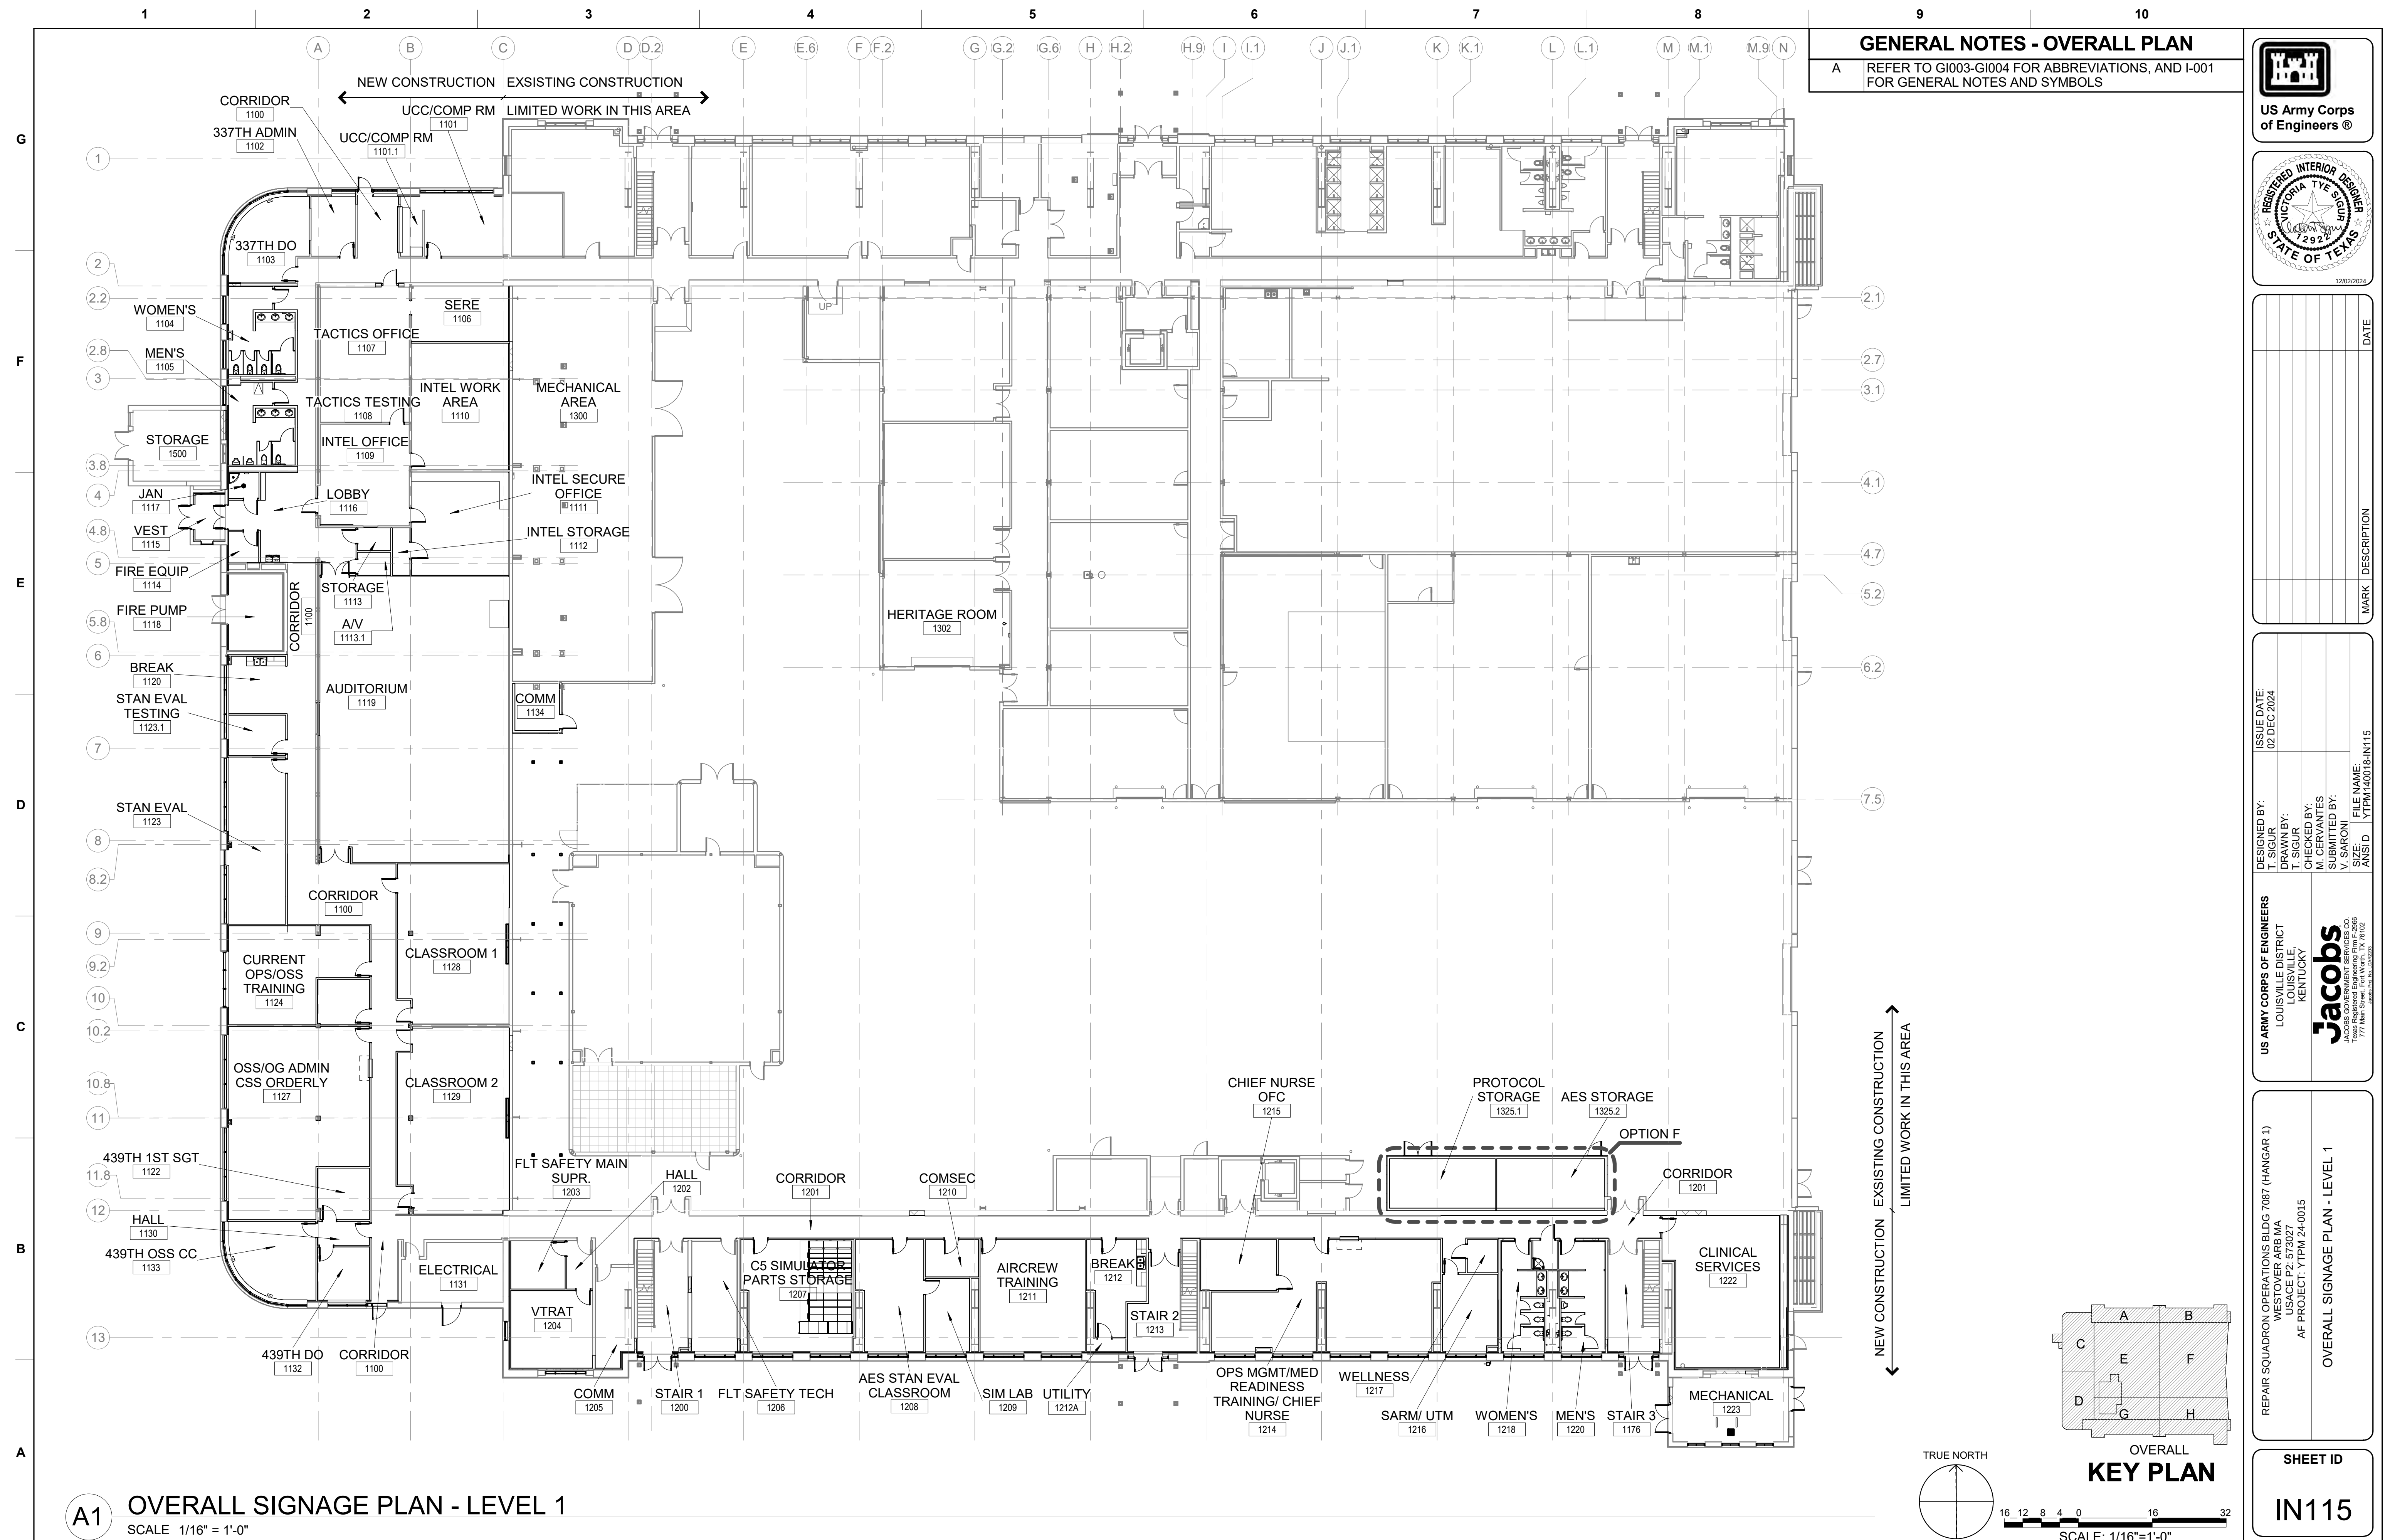


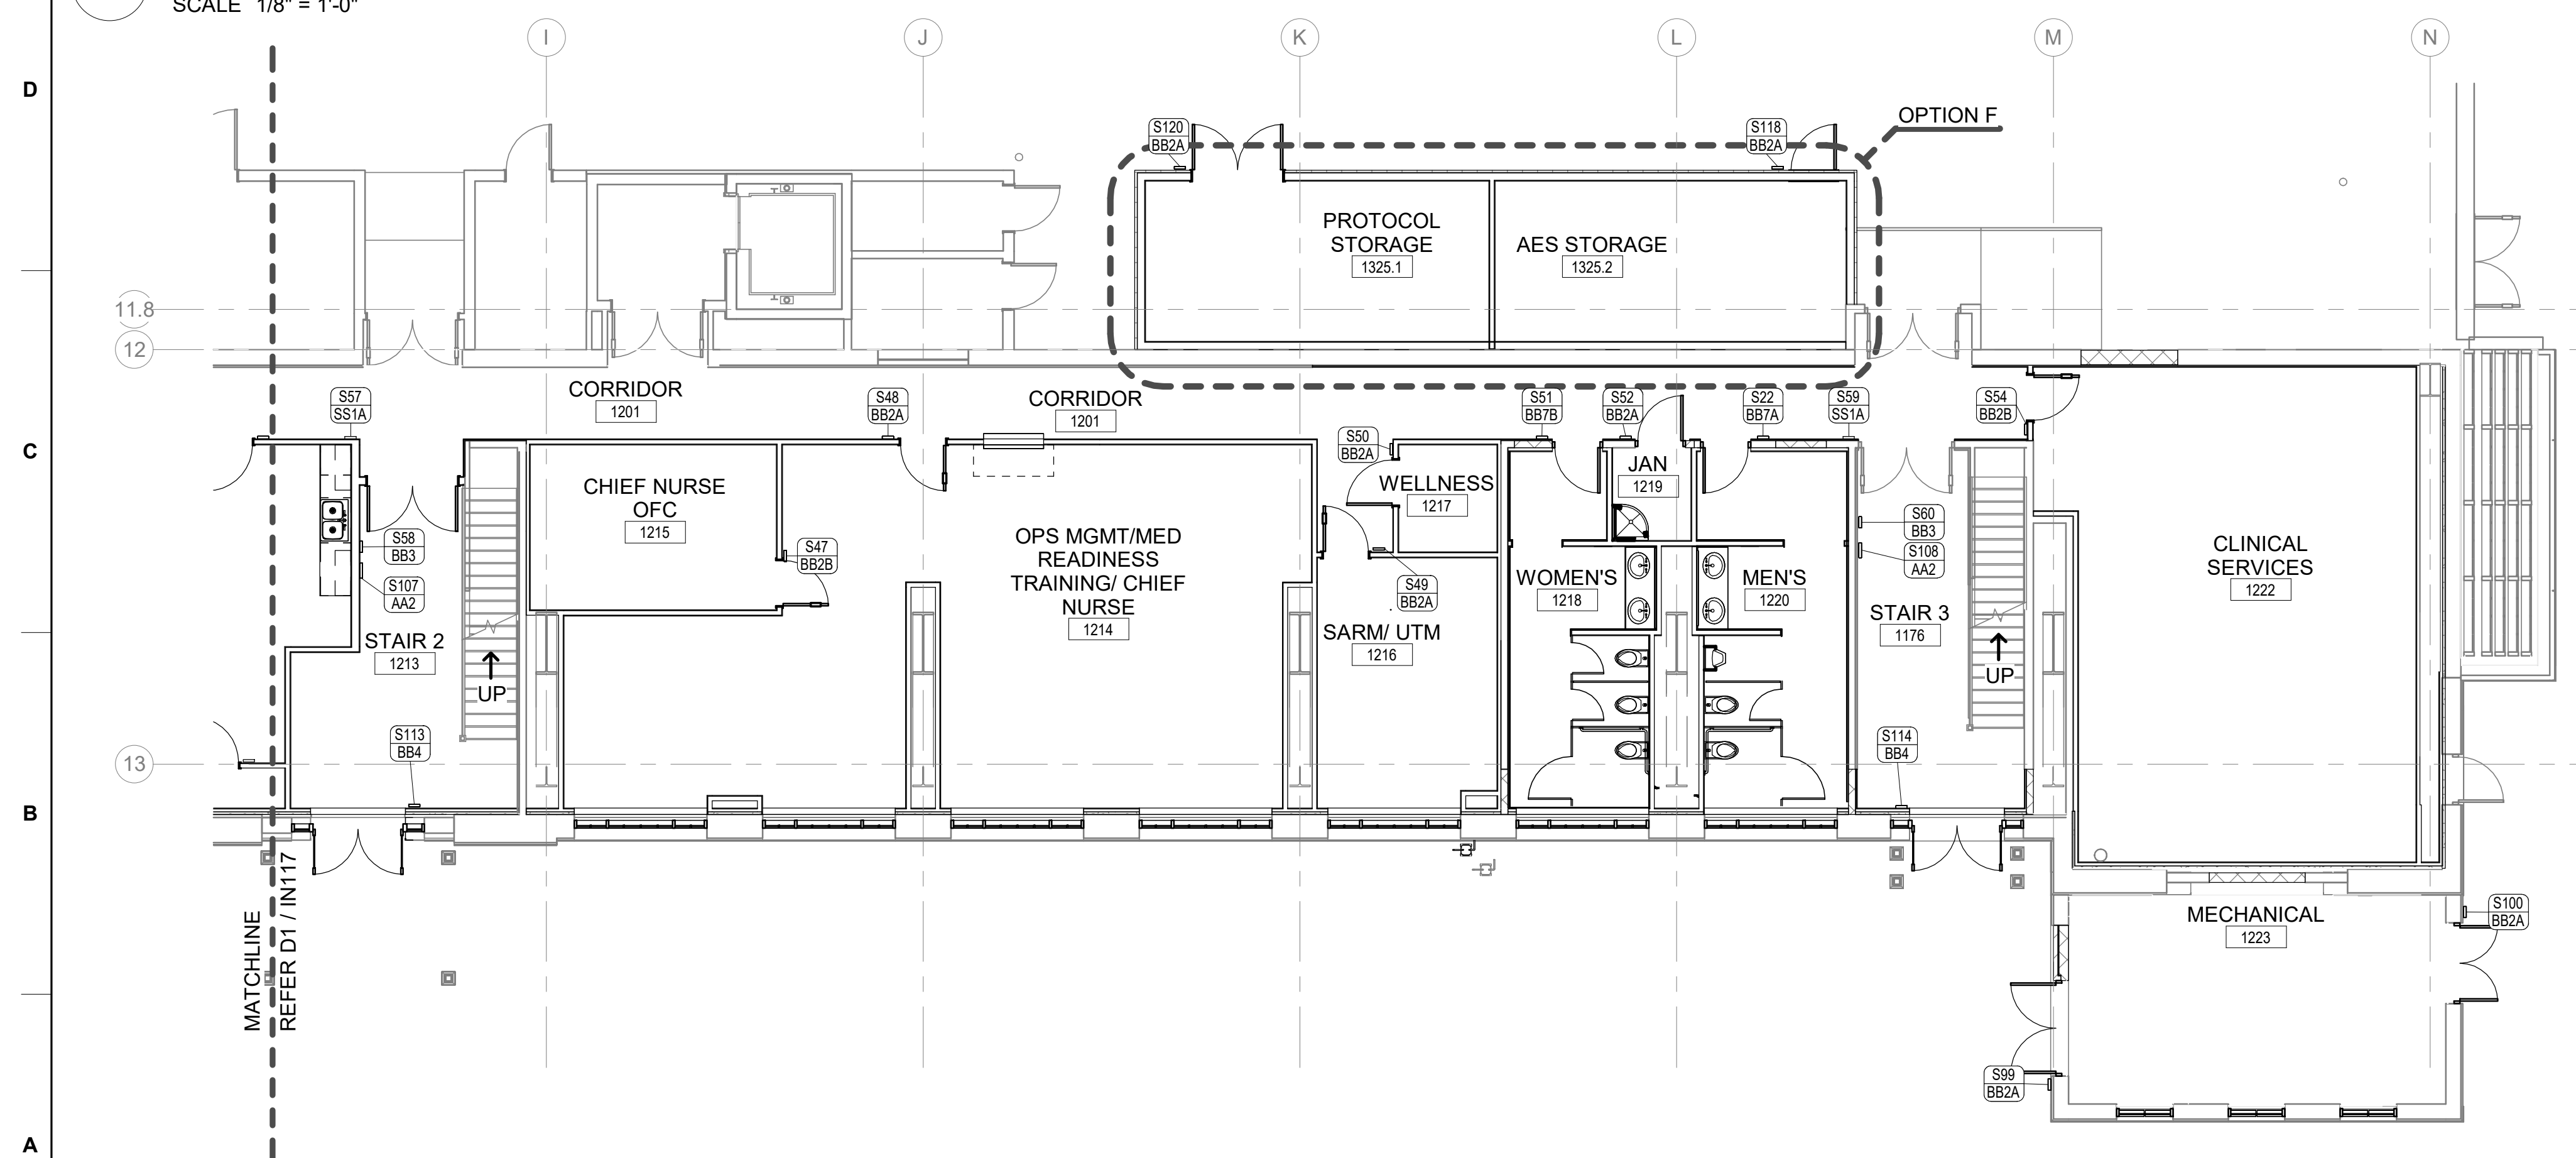


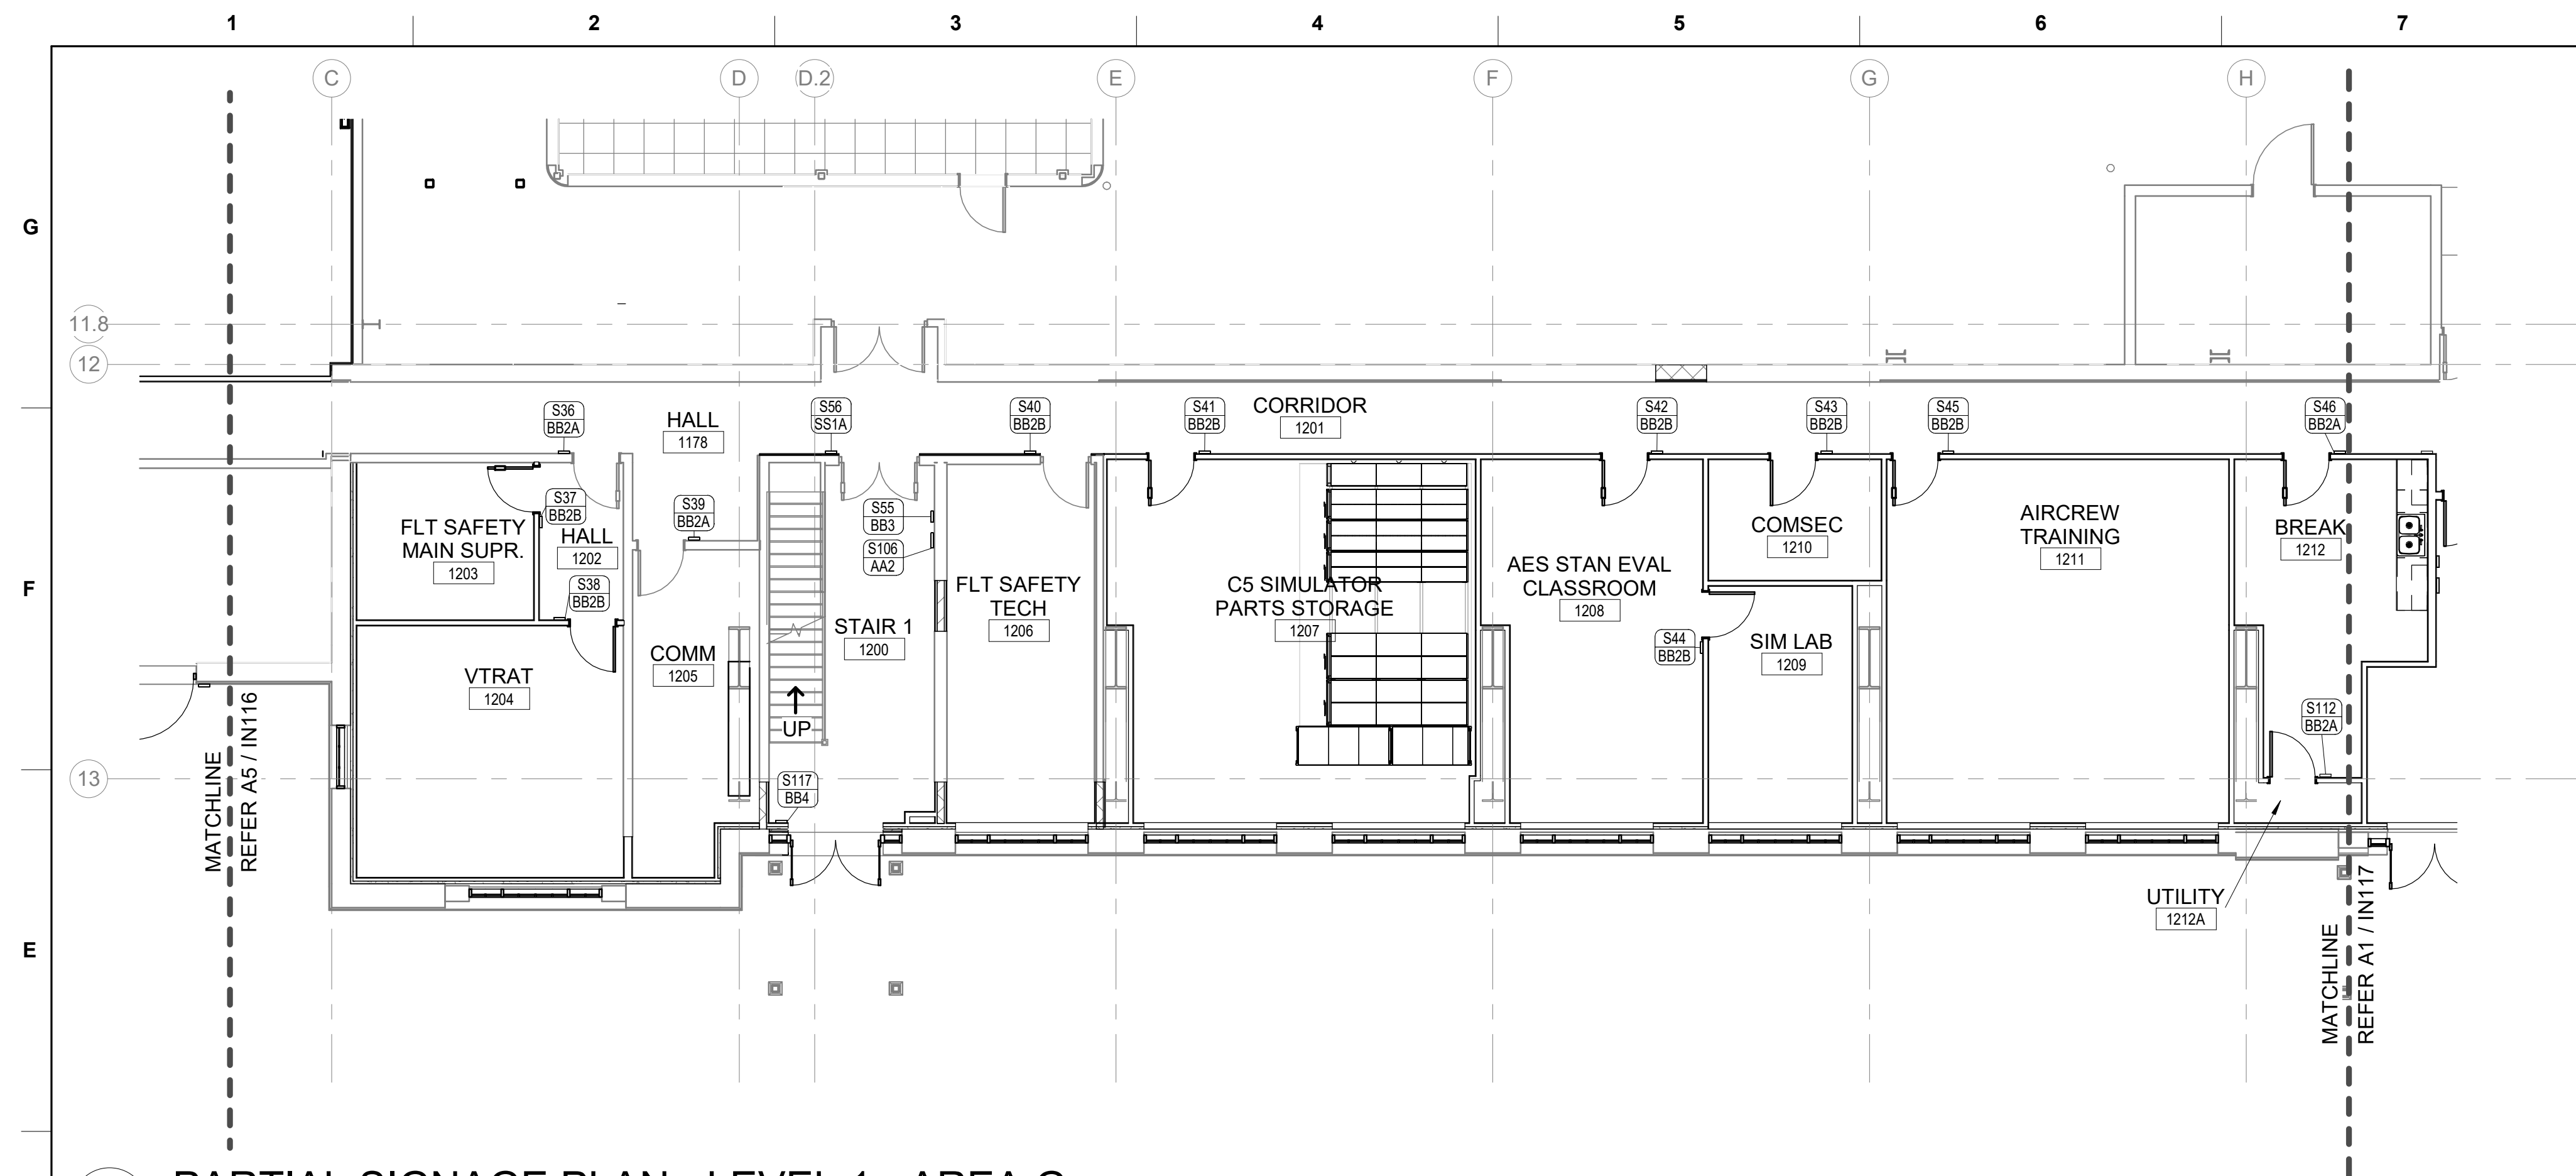


GENERAL NOTES - SIGNAGE PLANS

- | | |
|----|--|
| A. | ALL SIGNAGE MUST COMPLY WITH ABA & UFC 3 120 01 CRITERIA. |
| B. | COORDINATE ALL ROOM NUMBERS AND VERBIAGE FOR SIGNS WITH CONTRACTING OFFICER PRIOR TO FABRICATION. |
| C. | ENSURE THAT ALL SIGN INERTS CAN BE EASILY REMOVED/REPLACED. CONSIDER INSTALLATION OF SIGNS IN TIGHT CORNERS AND ALCOVES/SIDELIGHTS TO ENSURE THAT SIGN INSERT IS ACCESSIBLE. |
| D. | MOUNT ALL LIKE-SIGNS AT SAME HEIGHT. |
| E. | NEW SIGNAGE MUST MATCH EXISTING SIGNAGE IN PREVIOUS PHASES. |

SIGNAGE KEY

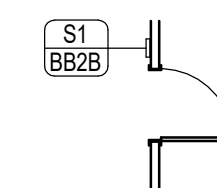



INDICATES SIGN MOUNTED ON WALL.
REFER TO I-510, I-511, & I-601

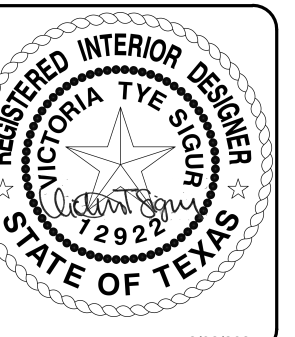[illegible]


 JACOBS GOVERNMENT SERVICES CO. 10000 E. Harvard Ave. Suite 100 Denver, CO 80231 (303) 752-1000		LOUISVILLE DISTRICT LOUISVILLE KENTUCKY	T. SIGUR DRAWN BY: 02 DEC 2024
C. SIGUR CHECKED BY: M. CERVANTES SUBMITTED BY: V. SARONI		FILE NAME: SIZE: ANSD FILEPATH:40018-IN1-17	



PARTIAL SIGNAGE PLAN - LEVEL 1 -
AREAS G AND H

SHEET ID
IN117

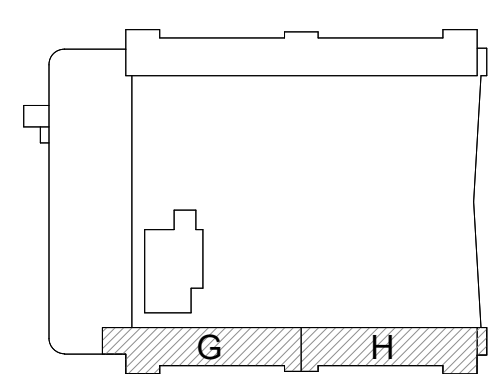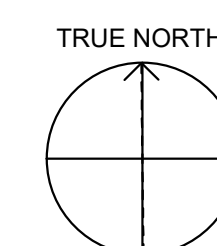

KEY PLAN

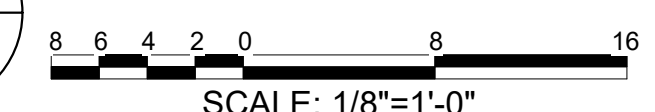


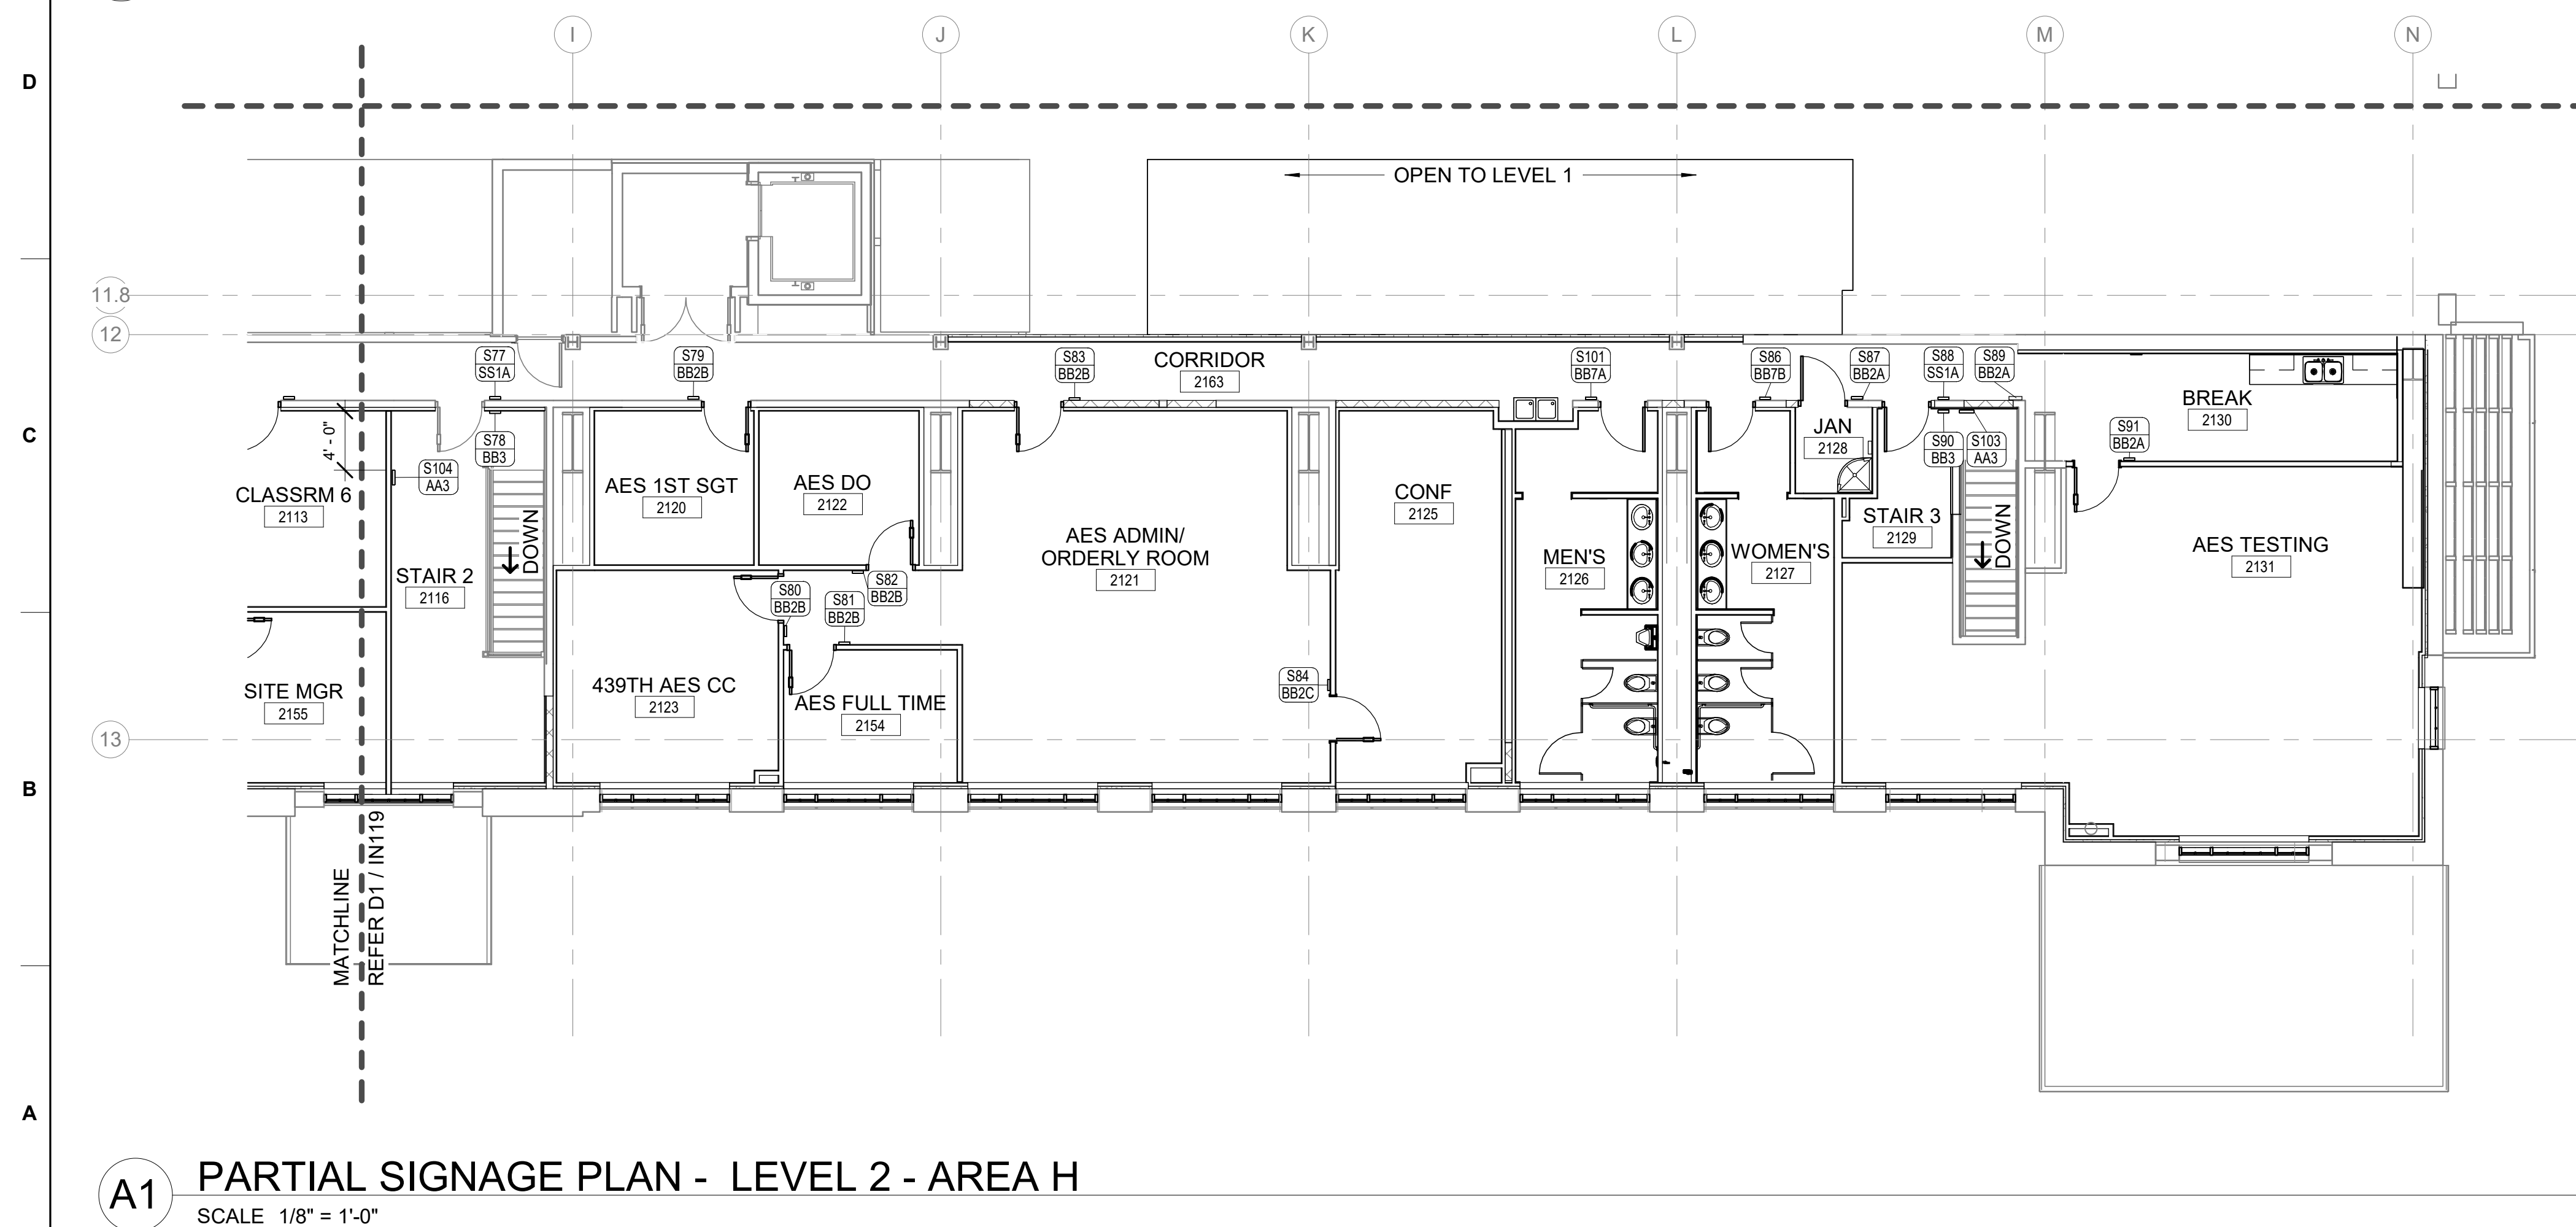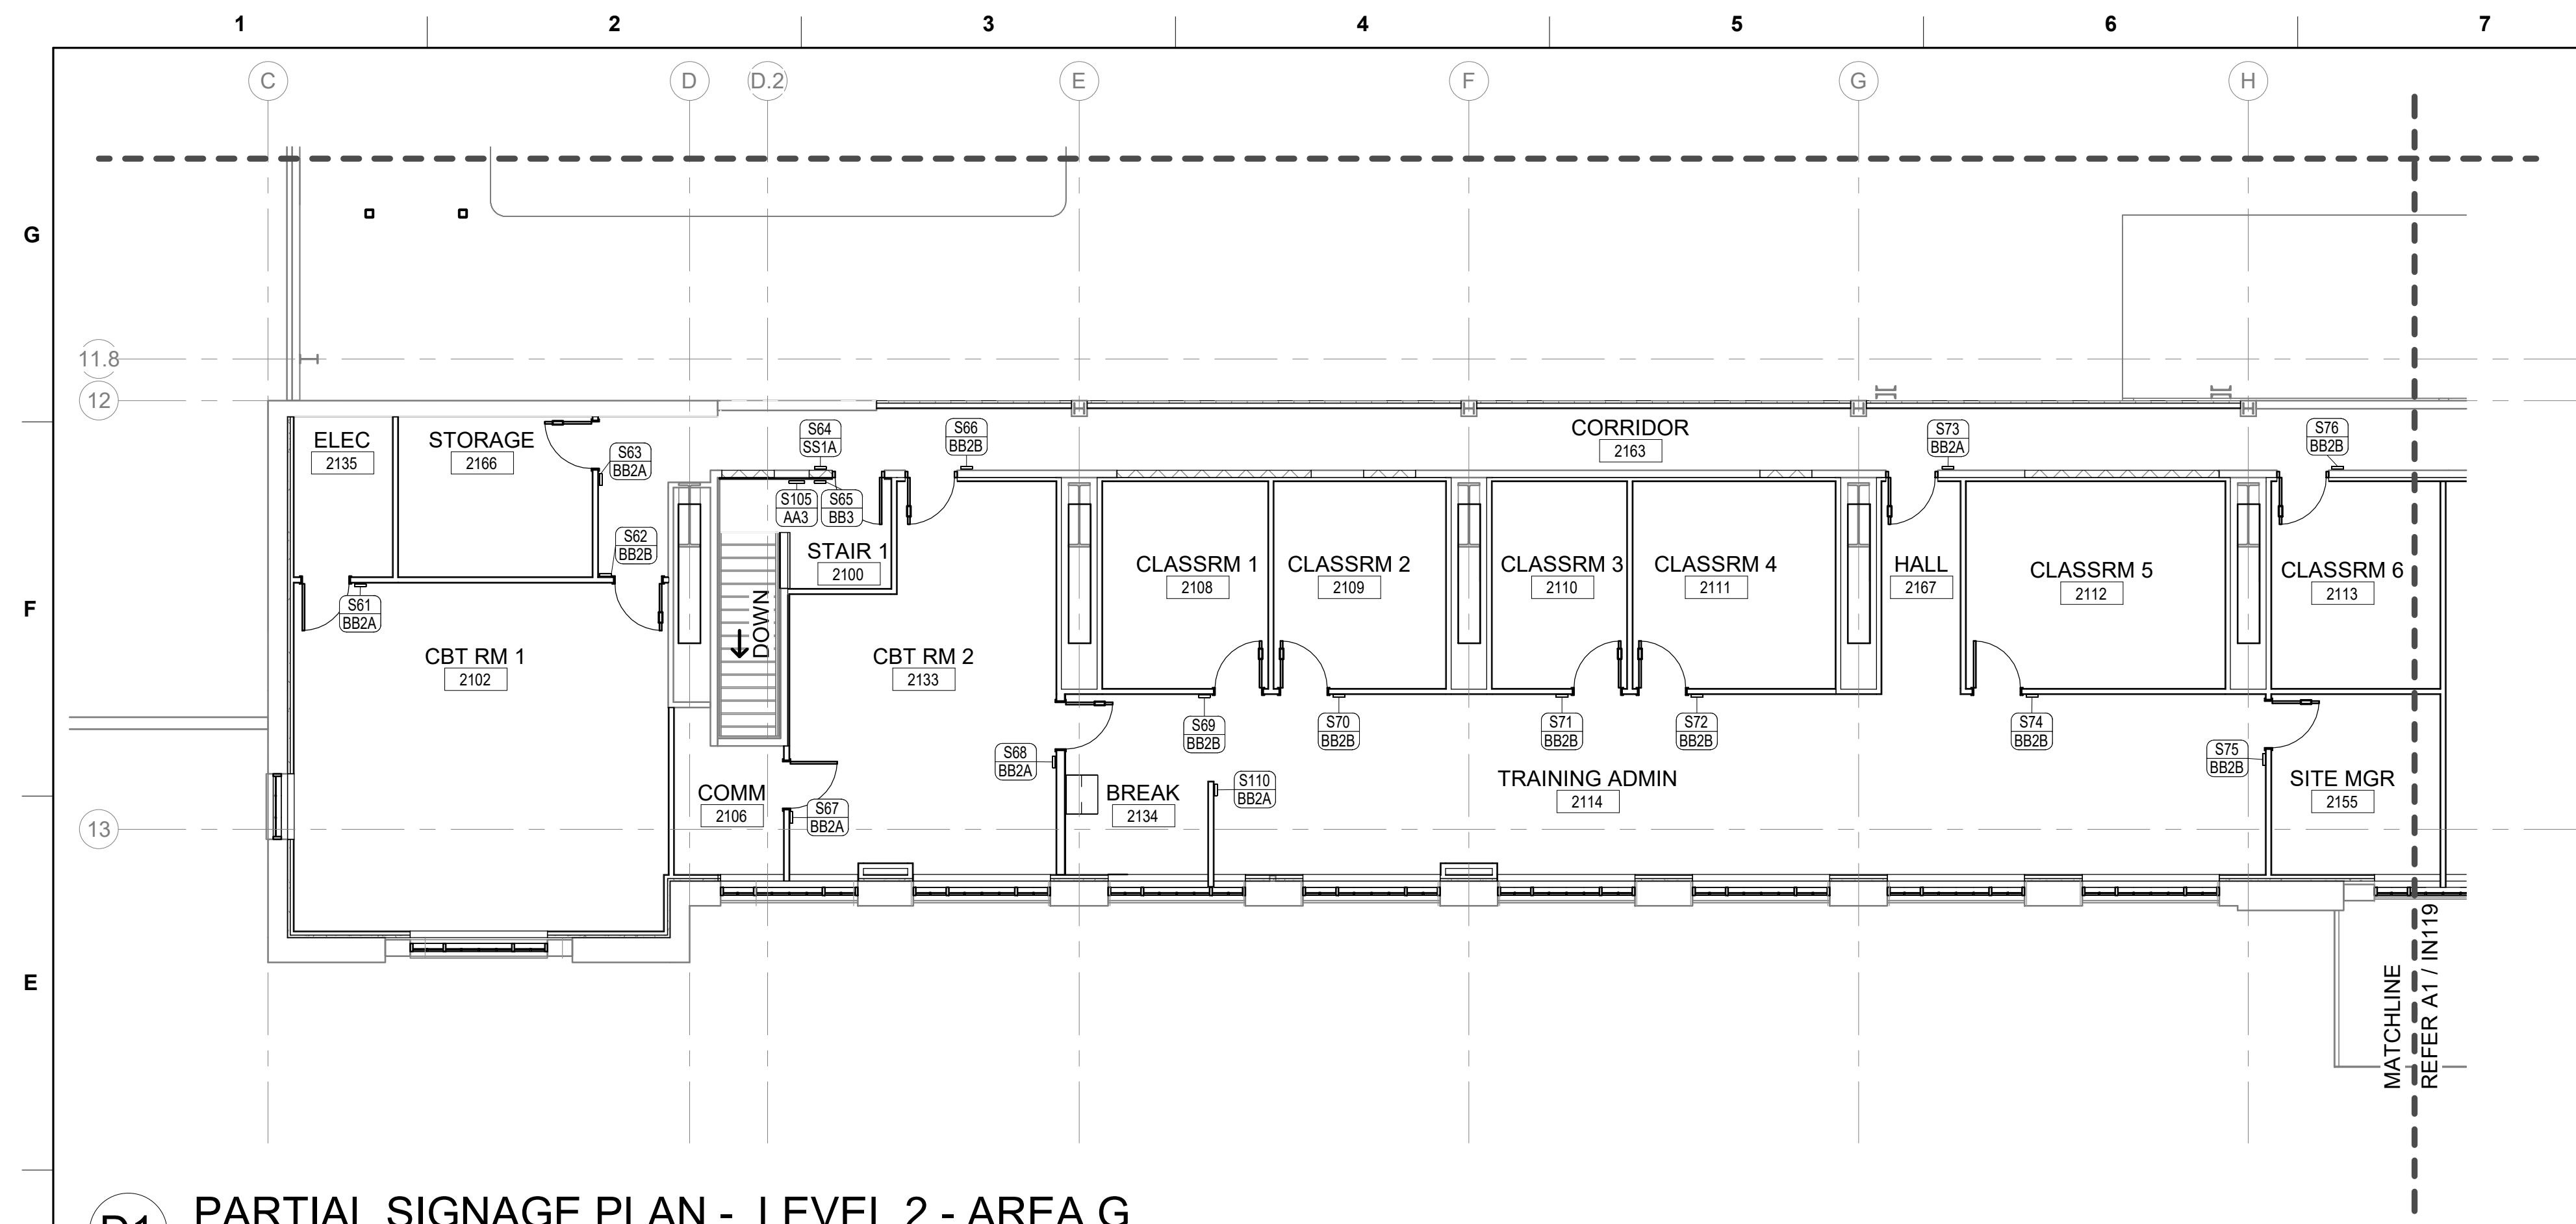

GENERAL NOTES - SIGNAGE PLANS

- | | |
|----|--|
| A. | ALL SIGNAGE MUST COMPLY WITH ABA & UFC 3 120 01 CRITERIA. |
| B. | COORDINATE ALL ROOM NUMBERS AND VERBIAGE FOR SIGNS WITH CONTRACTING OFFICER PRIOR TO FABRICATION. |
| C. | ENSURE THAT ALL SIGN INERTS CAN BE EASILY REMOVED/REPLACED. CONSIDER INSTALLATION OF SIGNS IN TIGHT CORNERS AND ALCOVES/SIDELIGHTS TO ENSURE THAT SIGN INSERT IS ACCESSIBLE. |
| D. | MOUNT ALL LIKE-SIGNS AT SAME HEIGHT. |
| E. | NEW SIGNAGE MUST MATCH EXISTING SIGNAGE IN PREVIOUS PHASES. |

INDICATES SIGN MOUNTED ON WALL.
REFER TO I-510, I-511, & I-601

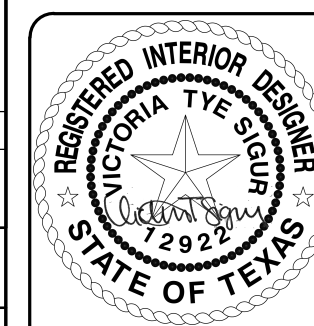US Army Corps
of Engineers®

12/02/2

[illegible][illegible]

DESIGNED BY:	ISSUE DATE:
--------------	-------------

DESIGNED BY:

DESIGNED BY:

DESIGNED BY:

DESIGNED BY:

DESIGNED BY:

US ARMY CORPS OF ENGINEERS

US ARMY CORPS OF ENGINEERS

REPAIR SQUADRON OPERATIONS BLDG 7087 (HANGAR 1)

SQUADRON OPERATIONS BLDG 7087 (HANGAR)


SHEET 11

IN119








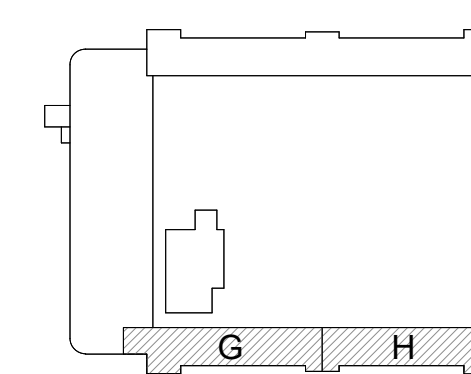


AREAS G&H

KEY PLAYS

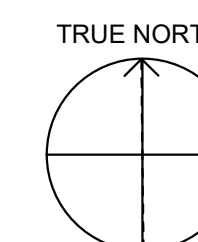

8 6 4 2 0 8
SCALE: 1/8"=1'-0"

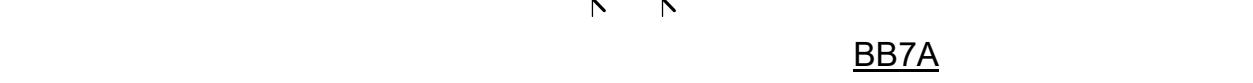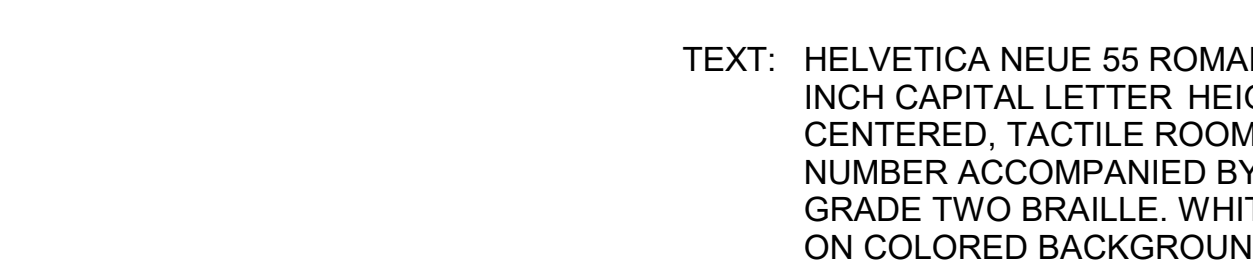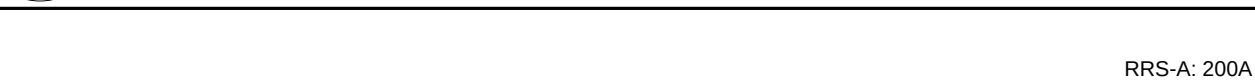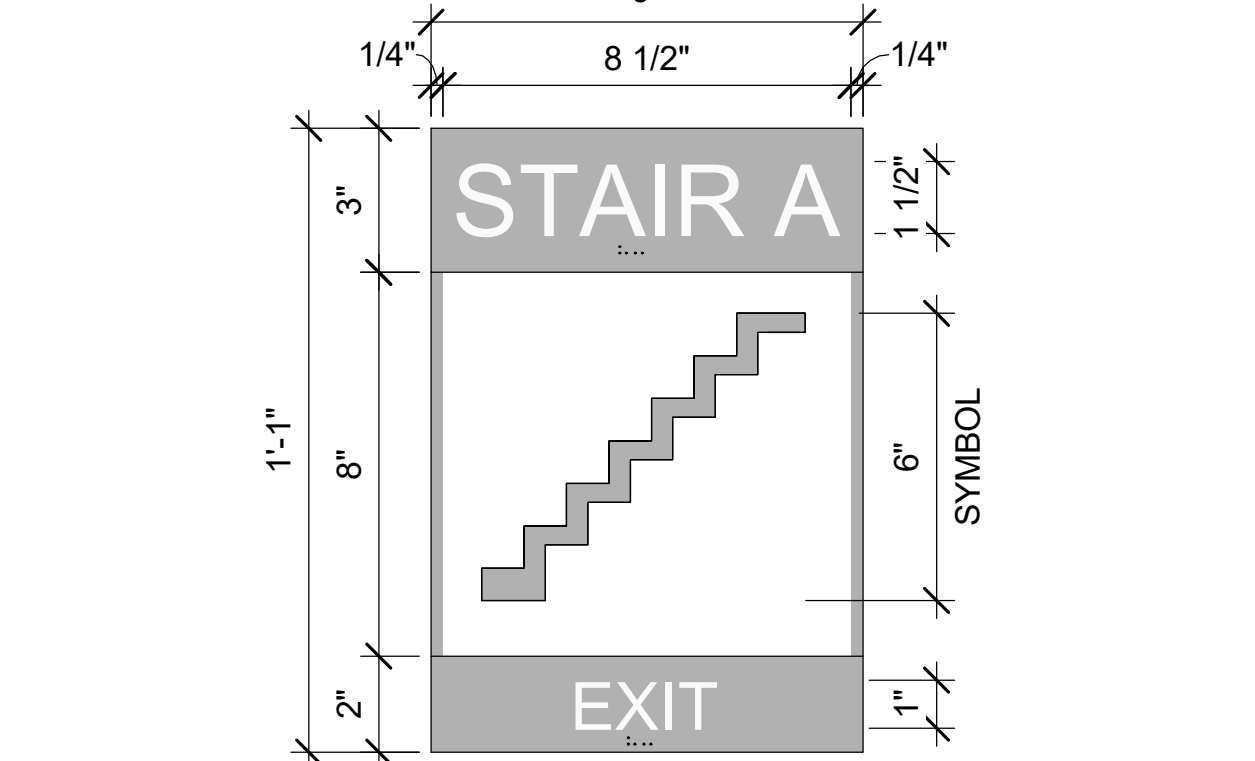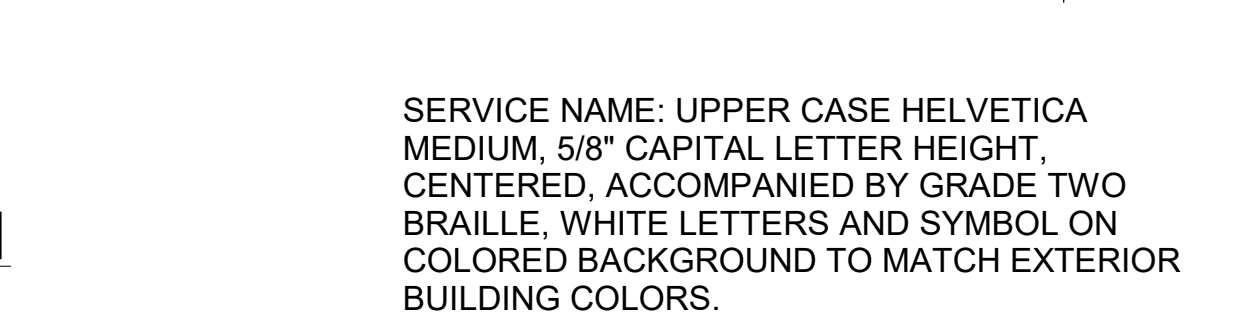 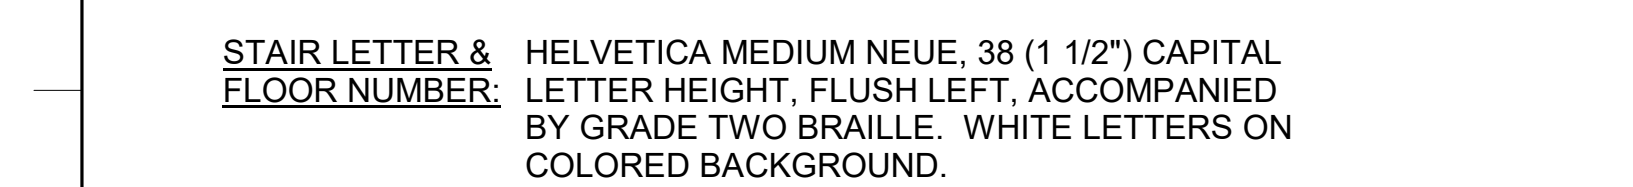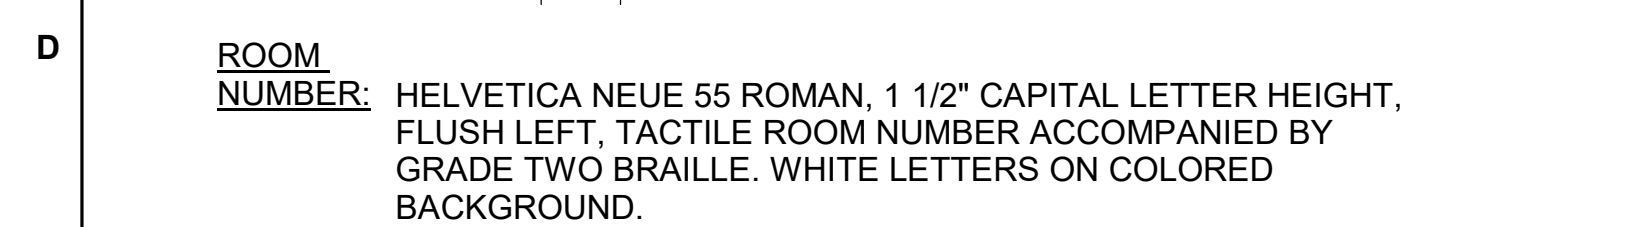

100

100

WHITE LETTERS

CEP

